
Piping & Instrumentation Diagram

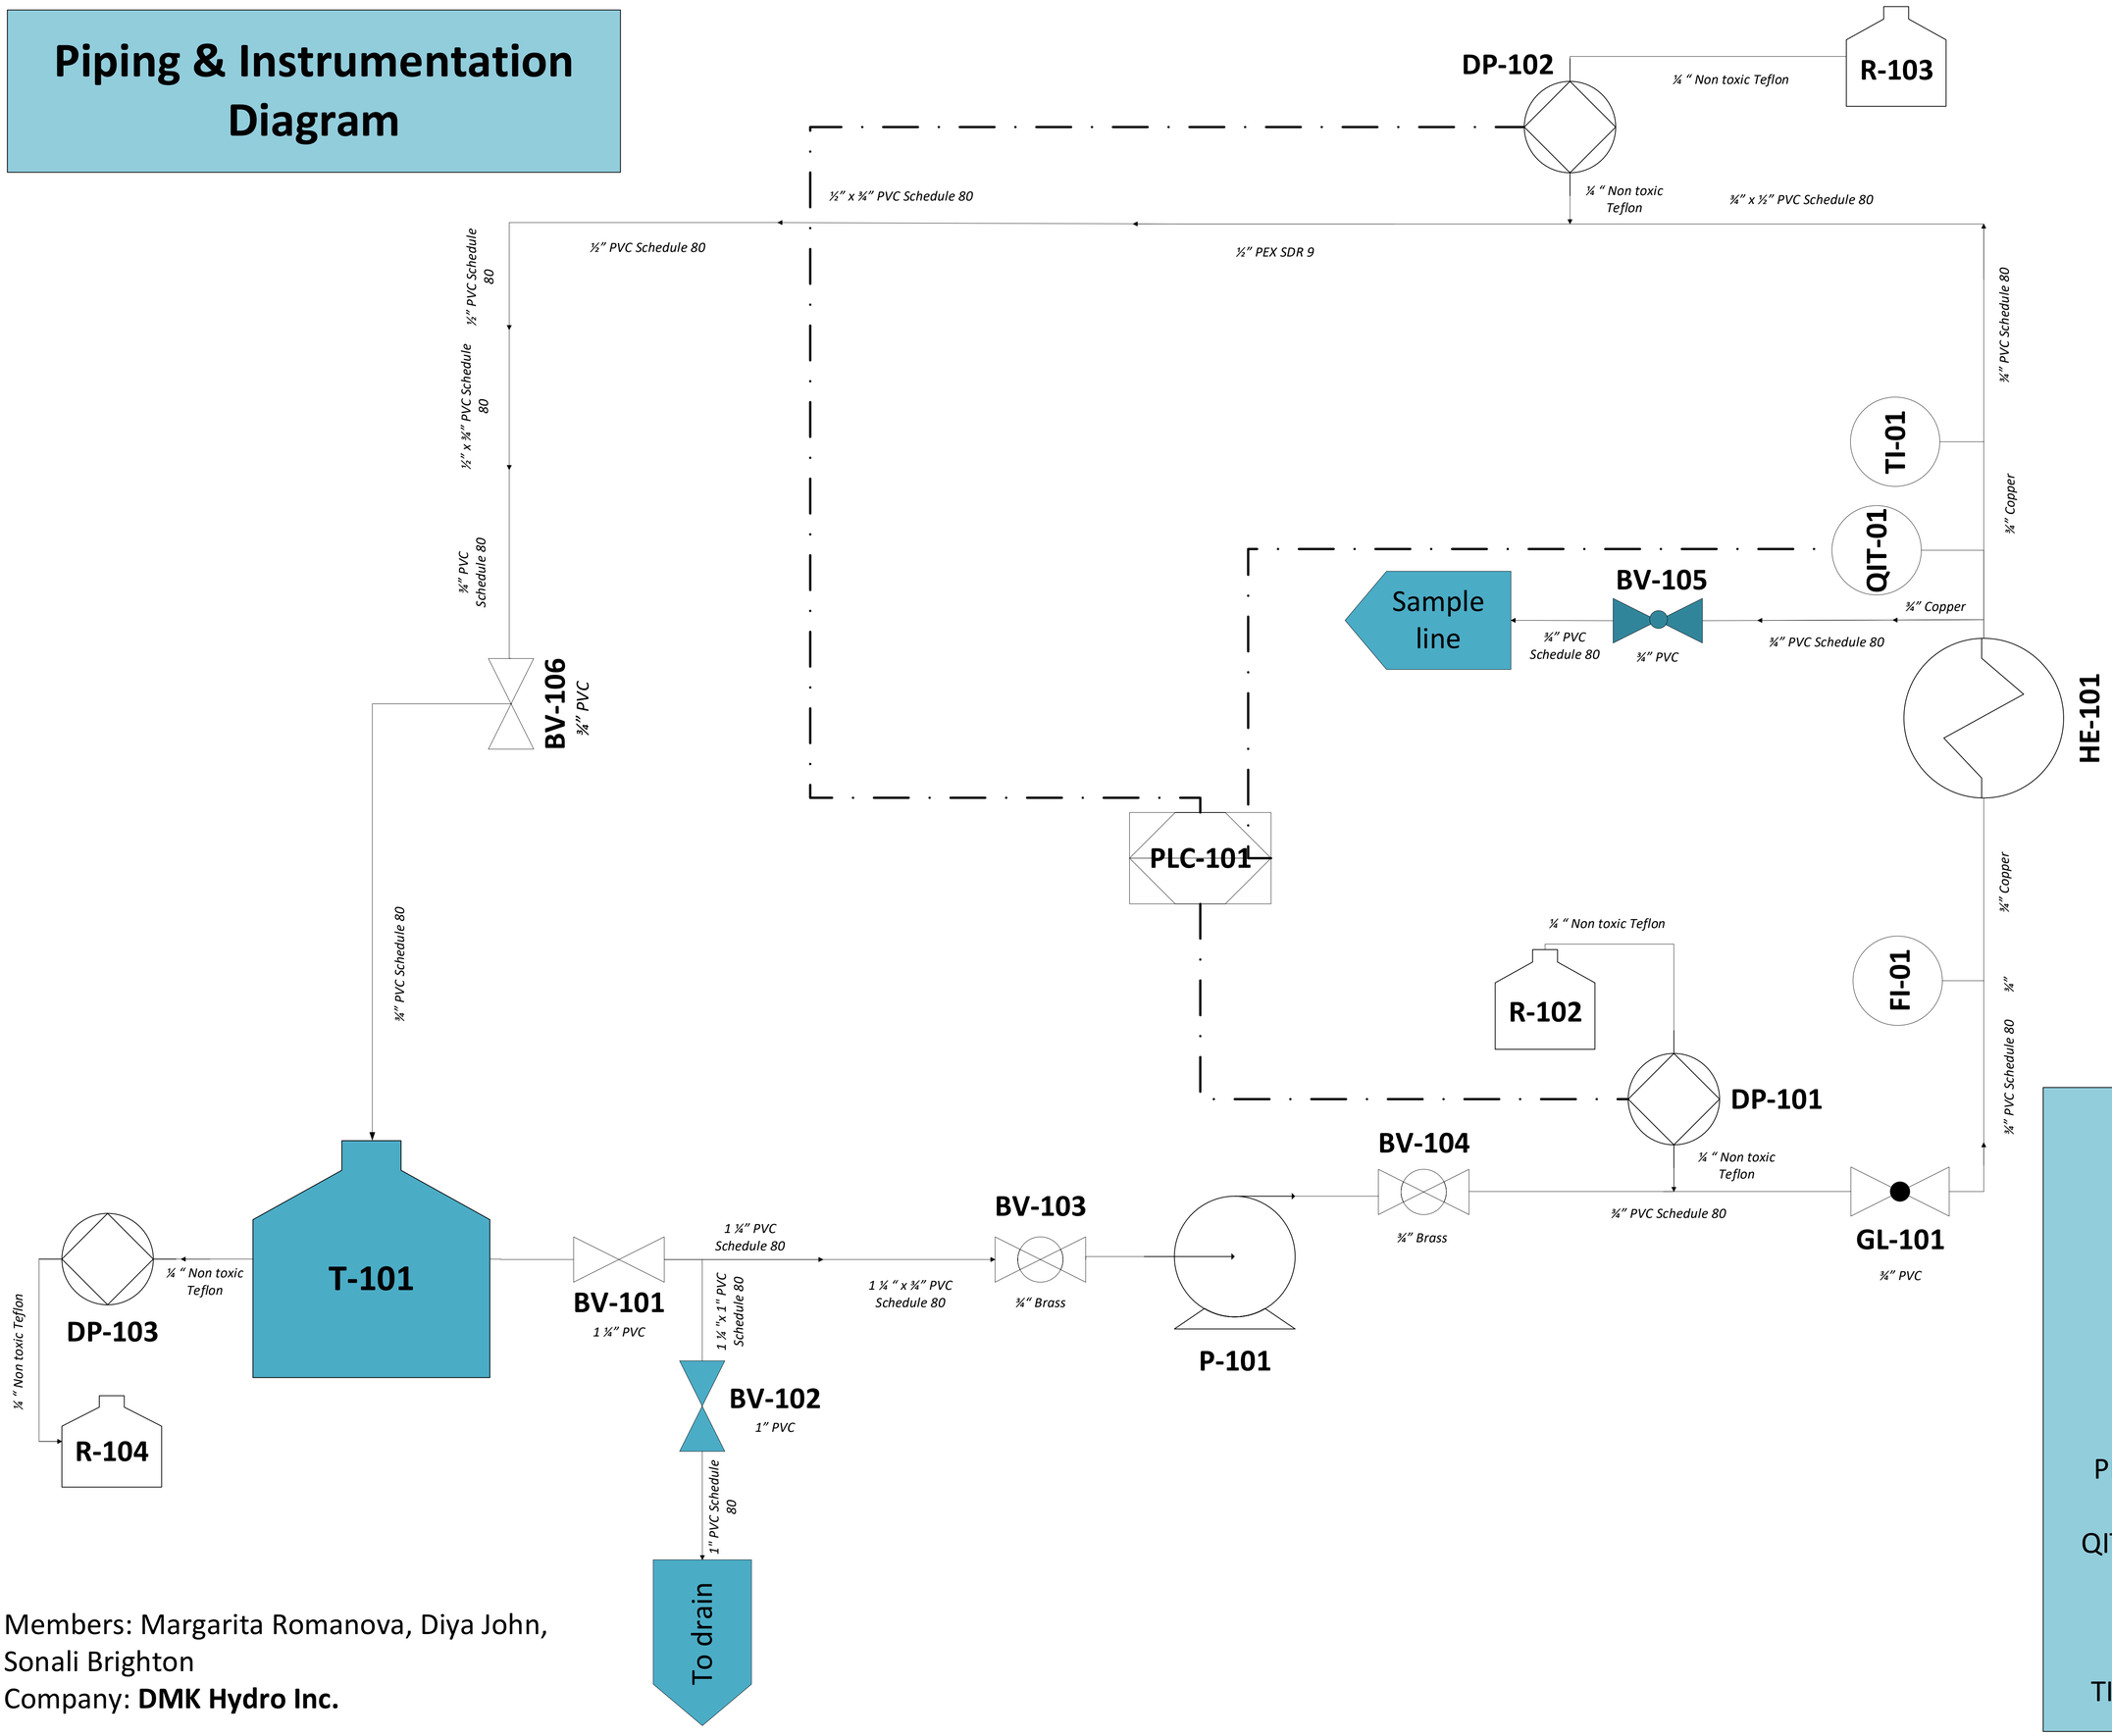

Members: Margarita Romanova, Diya John, Sonali Brighton

Company: **DMK Hydro Inc.**

LEGEND:

BV – Ball Valve
CV – Check Valve
CP – Centrifugal Pump
DP – Diaphragm Pump
FI – Flow Indicator
GL – Globe Valve
GV – Gate Valve
HE – Heat Exchanger
PLC – Programmable Logic Controller
QIT – Quantity Indicator and Transmitter
R – Reservoir
T – Main Mixing Tank
TI – Temperature Indicator